


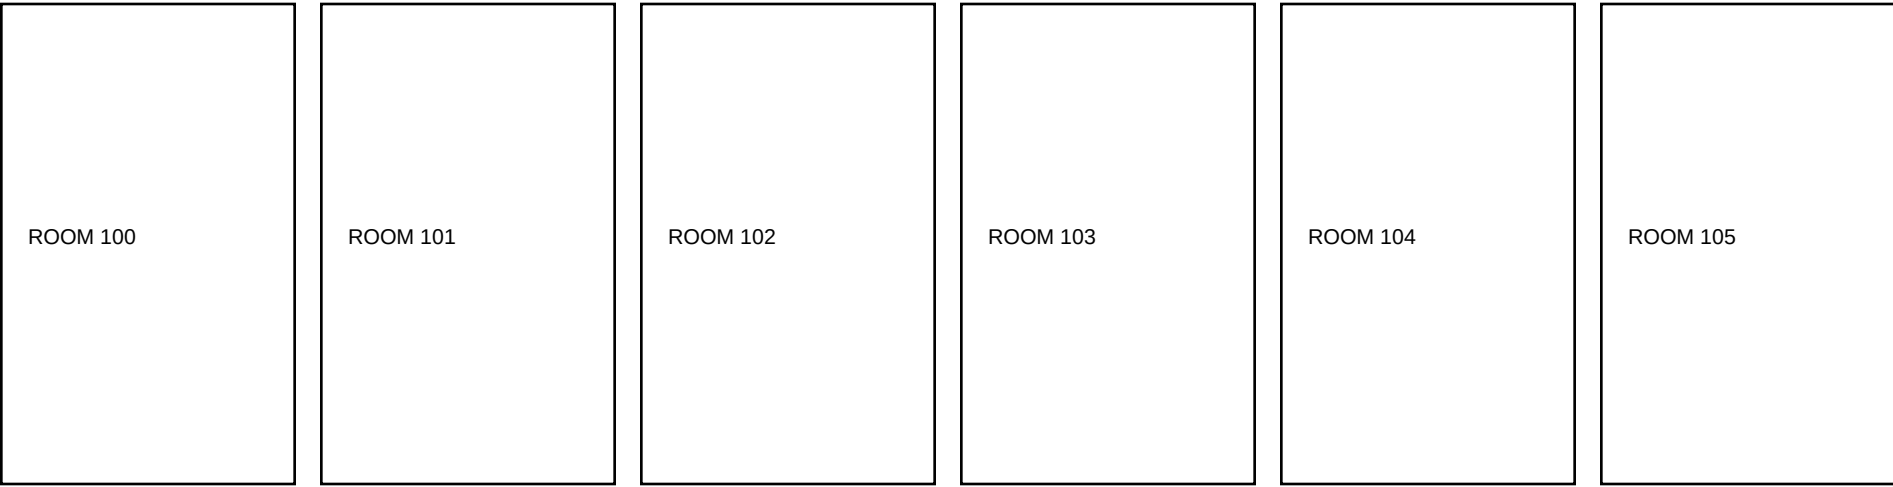


HOLABIRD ACADEMY RENOVATION

COVER SHEET AND DRAWING INDEX

SHEET NUMBER

G-001

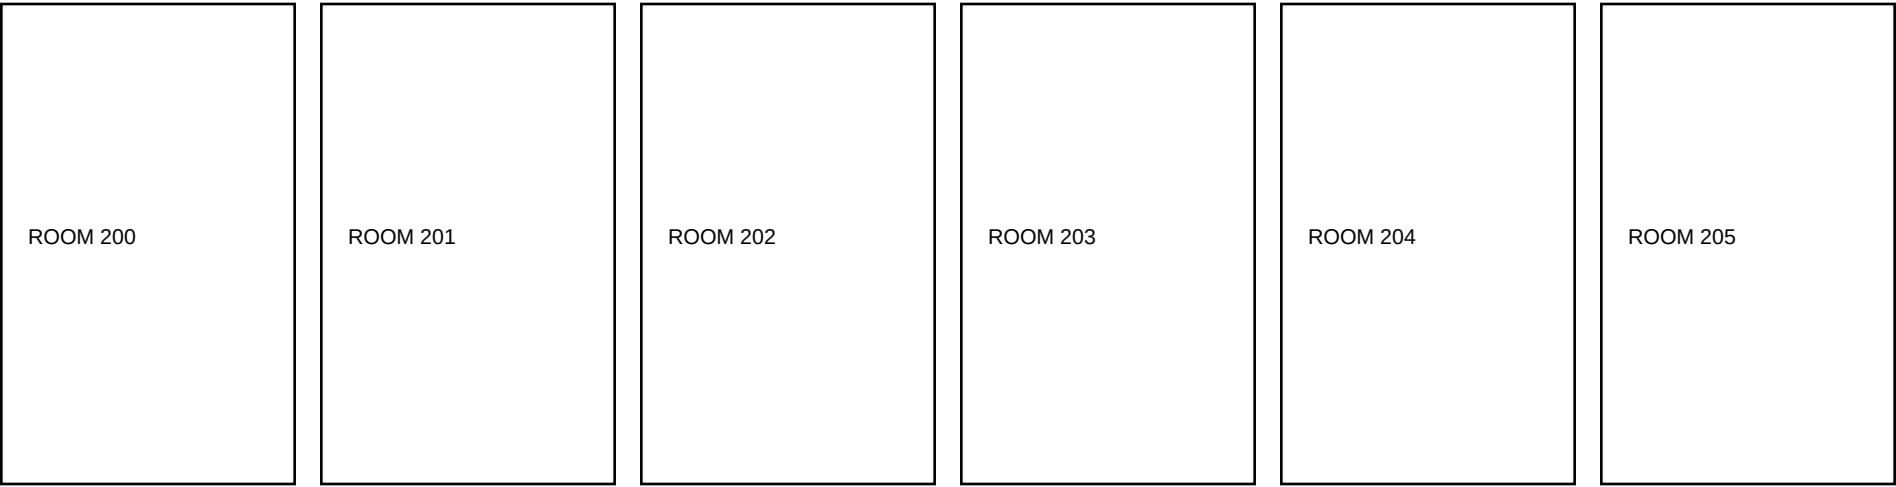


HOLABIRD ACADEMY RENOVATION

FIRST FLOOR PLAN

SHEET NUMBER

A-101

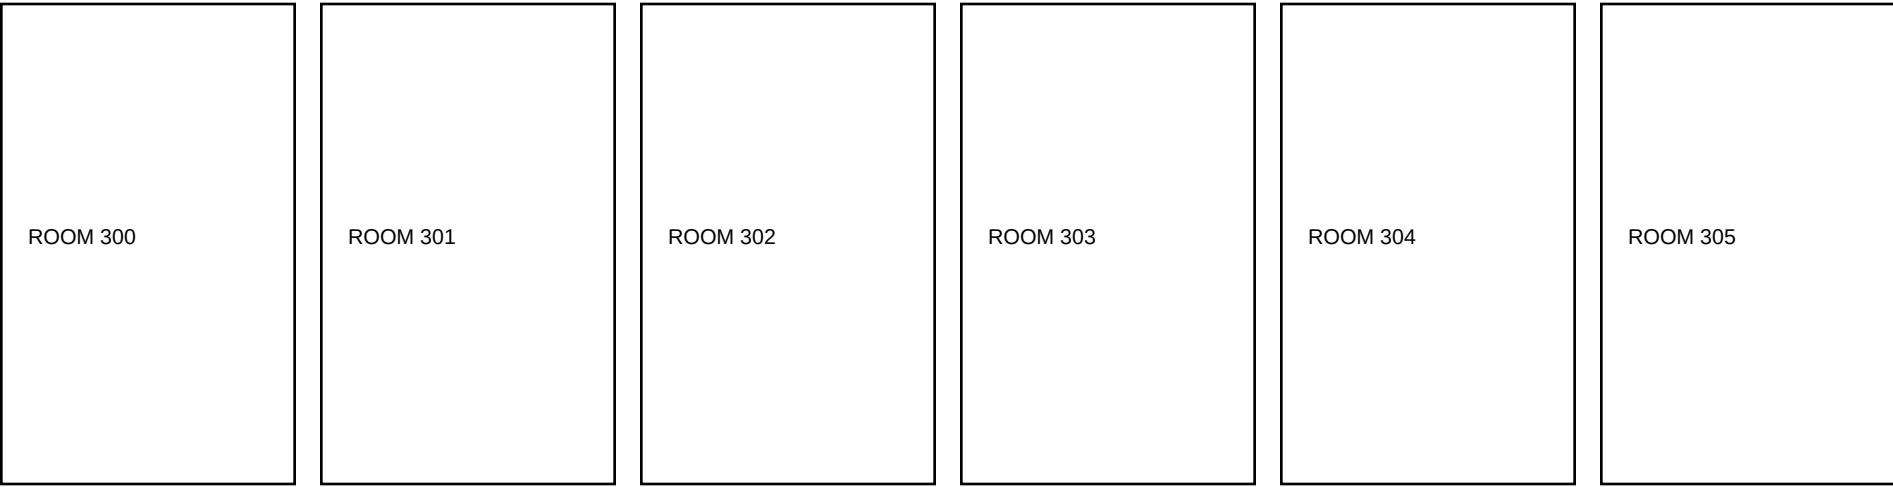


HOLABIRD ACADEMY RENOVATION

SECOND FLOOR PLAN

SHEET NUMBER

A-201

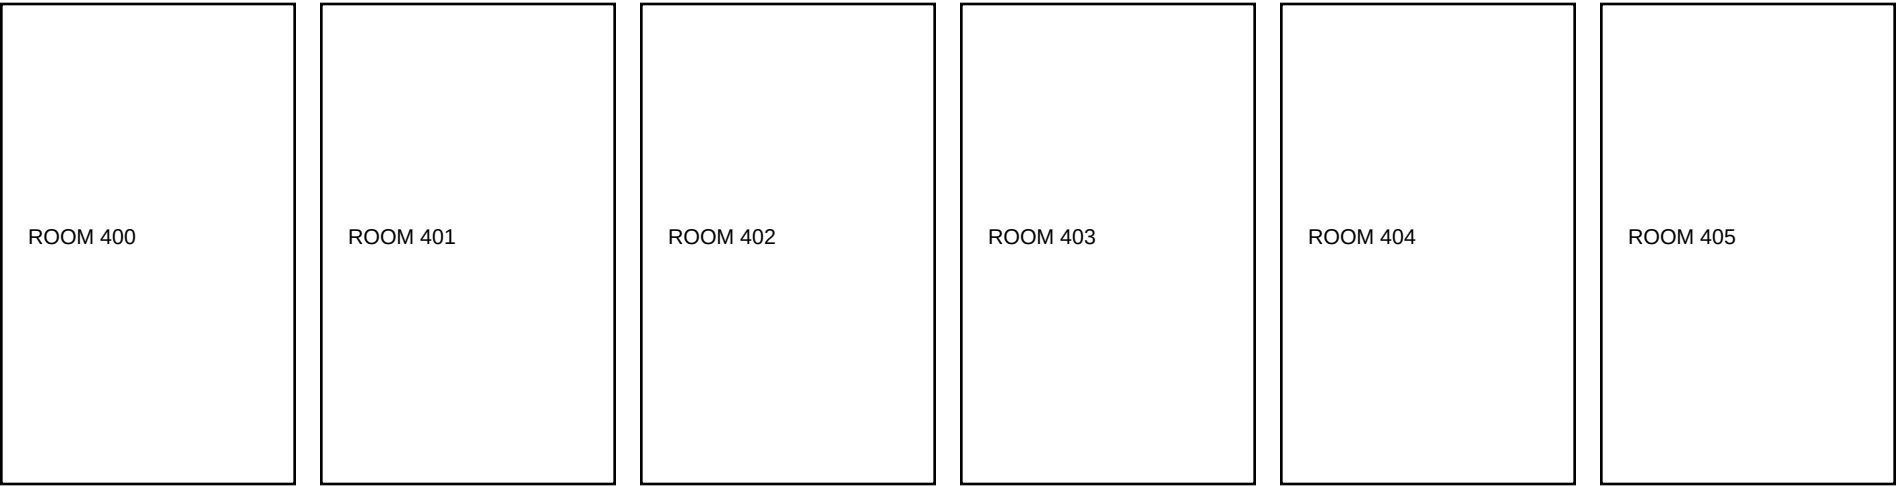

HOLABIRD ACADEMY RENOVATION

FOUNDATION PLAN

SHEET NUMBER

S-101